CROQUIS SEGÚN TÍTULO S/E

Nota: no consigna medidas lineales

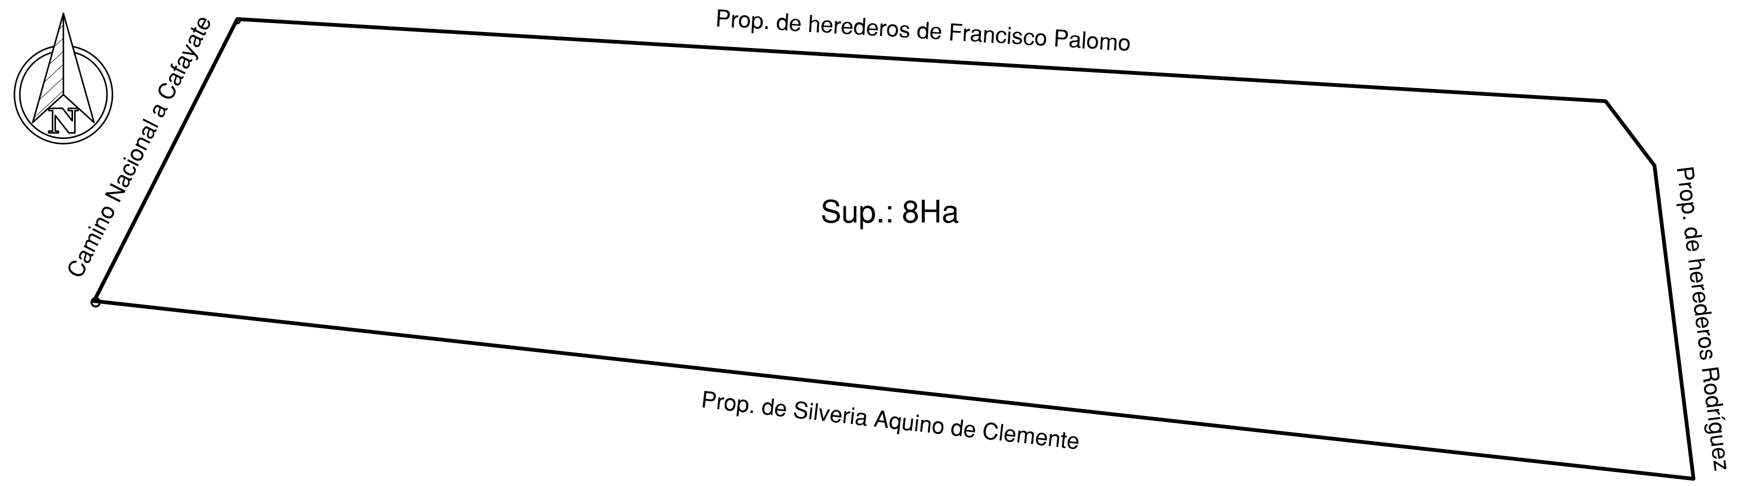
Prop. de herederos de Francisco Palomo
Camino Nacional a Cafayate
Sup.: 8Ha
Prop. de herederos Rodriguez
Prop. de Silveria Aquino de Clemente

DETALLE DE SUPERFICIES

SUP. TOTAL LOTES S/M 5Ha 2995,73m²
SUP. TOTAL RECREACIÓN ACTIVA S/M 4051,64m²
SUP. TOTAL RECREACIÓN PASIVA S/M 3515,01m²
SUP. CIRCULACIONES S/M 1Ha 8033,15m²

SUP. TOTAL S/M 7Ha 8595,53m²

BALANCE DE SUPERFICIES

SUP. TOTAL S/M 7Ha 8595,53m²
SUP. S/T MAT. 552 .... 8Ha 0000,00m²

DIFERENCIA EN (-) 1404,47m²

Propietario

Propietario

Certifico que las firmas que anteceden son auténticas de:
AGUIRRE, CECILIA CARMEN DNI: 29.545.923
MENDEZ, EMILIA GRACIELA DNI: 34.244.488
que han sido puestas en mi presencia y que corresponden a las actas N° ____________ folio N° ________ del libro de registro de firmas N° __________ y foja de certificación N° ______ .

Salta, _____ de __________ de 202__ .-

Profesional

Escribano

COORDENADAS GAUSS KRÜGER

VT	ESTE	NORTE
1	3507292,812	7134861,545
2	3507312,176	7134836,016
3	3507327,663	7134711,746
4	3506693,110	7134782,286
5	3506749,904	7134894,150

ANGULOS INTERNOS

VERTICE	
1	130°37'04"
2	149°55'21"
3	76°33'11"
4	69°25'34"
5	113°28'49"

NOTAS:

- La presente mensura fue vinculada a la Estación Permanente Trancas por el método NTRIP (RTK) - Marco de Referencia POSGAR 07.

REFERENCIAS

— Línea de Mensura
–×–×– Alambrado (ZC)
○ Postes de Madera

Salta, Marzo de 2024

PLANO DE MENSURA, SUBDIVISIÓN PARA URBANIZACIÓN RESIDENCIAL PRIVADO

DEPARTAMENTO: SAN CARLOS

LOCALIDAD: EL BARRIAL

URBANIZACIÓN: "DON BORROMEO"

PROPIETARIOS: AGUIRRE, CECILIA CARMEN
MENDEZ, EMILIA GRACIELA

TÍTULO INSCRIPTO EN: Cédula Parcelaria

NOMENCLATURA CATASTRAL: MAT.: 552

ANTECEDENTES GRÁFICOS: LÁMINA CATASTRAL - PL. 69, 485 Y 700

CROQUIS DE UBICACIÓN

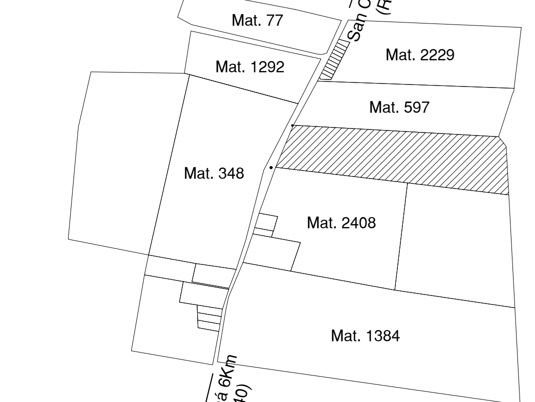

SELLADOS

VISADOS DE OTROS ORGANISMOS

D. G. DE INMUEBLES